Canberra-style store: blueprint

Drawn from the model's own constants (src/shared), so these pages cannot differ from the 3D scene. Metres. A visitor entering stands at the glass front facing the bar; the +x wall is on their left.

What the references say, and what changed

From the corners you set in the rectify tool (docs/blueprint/rectify.json) the references gave a shop about **10 m wide by 10 m deep** under a **3 m** wall (side walls 3.35 times as long as high, back wall 3.3 times as wide as high). You then asked for more room so the tables are spread out and people can move between them, and chose to keep the 3 m wall. The shop is now **11 m wide by 15.4 m deep by 3 m high**, so it is deliberately wider and much longer than the reference proportions.

Dimensions

Part	Value	Source
Shop width x depth x height	11 x 15.4 x 3 m	Your choice (option A): more room than the 10 x 10 m the references gave
Table columns	x = -2.8, 0, 2.8	About a quarter of the width either side of the middle (photo)
Product tables	1 wide x 1.2 long (almost square), four in each side column and three in the middle, one product on each side, 1.0 m clear between them front to back	Your description
Service tables	1.2 m square (the long edge of a product table), one nearest the bar in each side column and one in the middle column, two stools tucked under each of its left and right sides, no products	Your description
Bench along each side wall	0.56 m deep, 10.4 m long (it stops where the indented bays start), 0.95 m high	Your instruction, from the references
Ledges in front of the bays	one short ledge on the front half of each of the three bays on each side, 0.35 m out from the wall, one product on each	Which half and which product are [TK]: working defaults
Entrance clear zone	2.5 m from the glass to the first table, kept empty: customers are received here	Your instruction
Service bar	6.6 m long x 0.8 m deep, 1.05 m high, 13 stools tucked under the overhang	Almost from the far end of one service table to the far end of the other; 13 stools by your instruction
Staff door	1.0 m wide, left of the bar as you face it (+x)	Your description
Entrance opening	3 m wide, middle of the glass front	Assumed [TK]
Back room	15.4 m deep, same footprint, two shelving rows, two repair benches	Your instruction

Where the scale is uncertain

- **The 3 m wall height is the one absolute number.** The photographs fix the proportions; everything in metres follows from it. If the real ceiling is higher, the whole shop scales with it.
- Table length, the entrance opening and the back room are assumptions.
- Wall features (lightboxes, bays, monitors) are placed by their proportion of the wall in the close-up photographs.

Tables: position and orientation


Three columns across (the left column, the centre column and the right column as you enter). The **left and right columns** each have **four almost-square product tables** and, nearest the bar, a larger **square service table** with two stools on its left and two on its right, tucked under the table, where a customer can sit and talk with staff. The **centre column** has **three product tables and one square service table**. Product tables carry a product on each of their four sides, facing outward; service tables carry nothing. There is no true top-down photograph of the tables, so positions come from your description and the proportions of the reference photographs.

Table	Column	Kind	Centre x	Centre z	Size (x by z)	On it
T1	right column (the -x side)	product	-2.80	-4.60	1.00 x 1.20	phones, watches, earbuds
T2	right column (the -x side)	product	-2.80	-2.40	1.00 x 1.20	phones, watches, earbuds
T3	right column (the -x side)	product	-2.80	-0.20	1.00 x 1.20	phones, watches, earbuds
T4	right column (the -x side)	product	-2.80	2.00	1.00 x 1.20	phones, watches, earbuds
S1	right column (the -x side)	service (square)	-2.80	4.20	1.20 x 1.20	nothing: a table to sit and talk with staff, two stools each side tucked under it
T5	centre	product	0.00	-2.40	1.00 x 1.20	laptops, tablets, tablets with keyboards
T6	centre	product	0.00	-0.20	1.00 x 1.20	laptops, tablets, tablets with keyboards
T7	centre	product	0.00	2.00	1.00 x 1.20	laptops, tablets, tablets with keyboards
S2	centre	service (square)	0.00	4.20	1.20 x 1.20	nothing: a table to sit and talk with staff, two stools each side tucked under it
T8	left column (the +x side, as you enter)	product	2.80	-4.60	1.00 x 1.20	headphones, speakers, trackers, earbuds
T9	left column (the +x side, as you enter)	product	2.80	-2.40	1.00 x 1.20	headphones, speakers, trackers, earbuds
T10	left column (the +x side, as you enter)	product	2.80	-0.20	1.00 x 1.20	headphones, speakers, trackers, earbuds
T11	left column (the +x side, as you enter)	product	2.80	2.00	1.00 x 1.20	headphones, speakers, trackers, earbuds
S3	left column (the +x side, as you enter)	service (square)	2.80	4.20	1.20 x 1.20	nothing: a table to sit and talk with staff, two stools each side tucked under it

z is negative towards the glass front and positive towards the bar. A person standing at any side of a product table has a product in front of them; neighbouring sides are more than a metre apart.

Top-down plan: the shop and the staff-only back room


Floor plan, as a visitor sees it entering: +x wall on the LEFT, entrance at the bottom (metres)

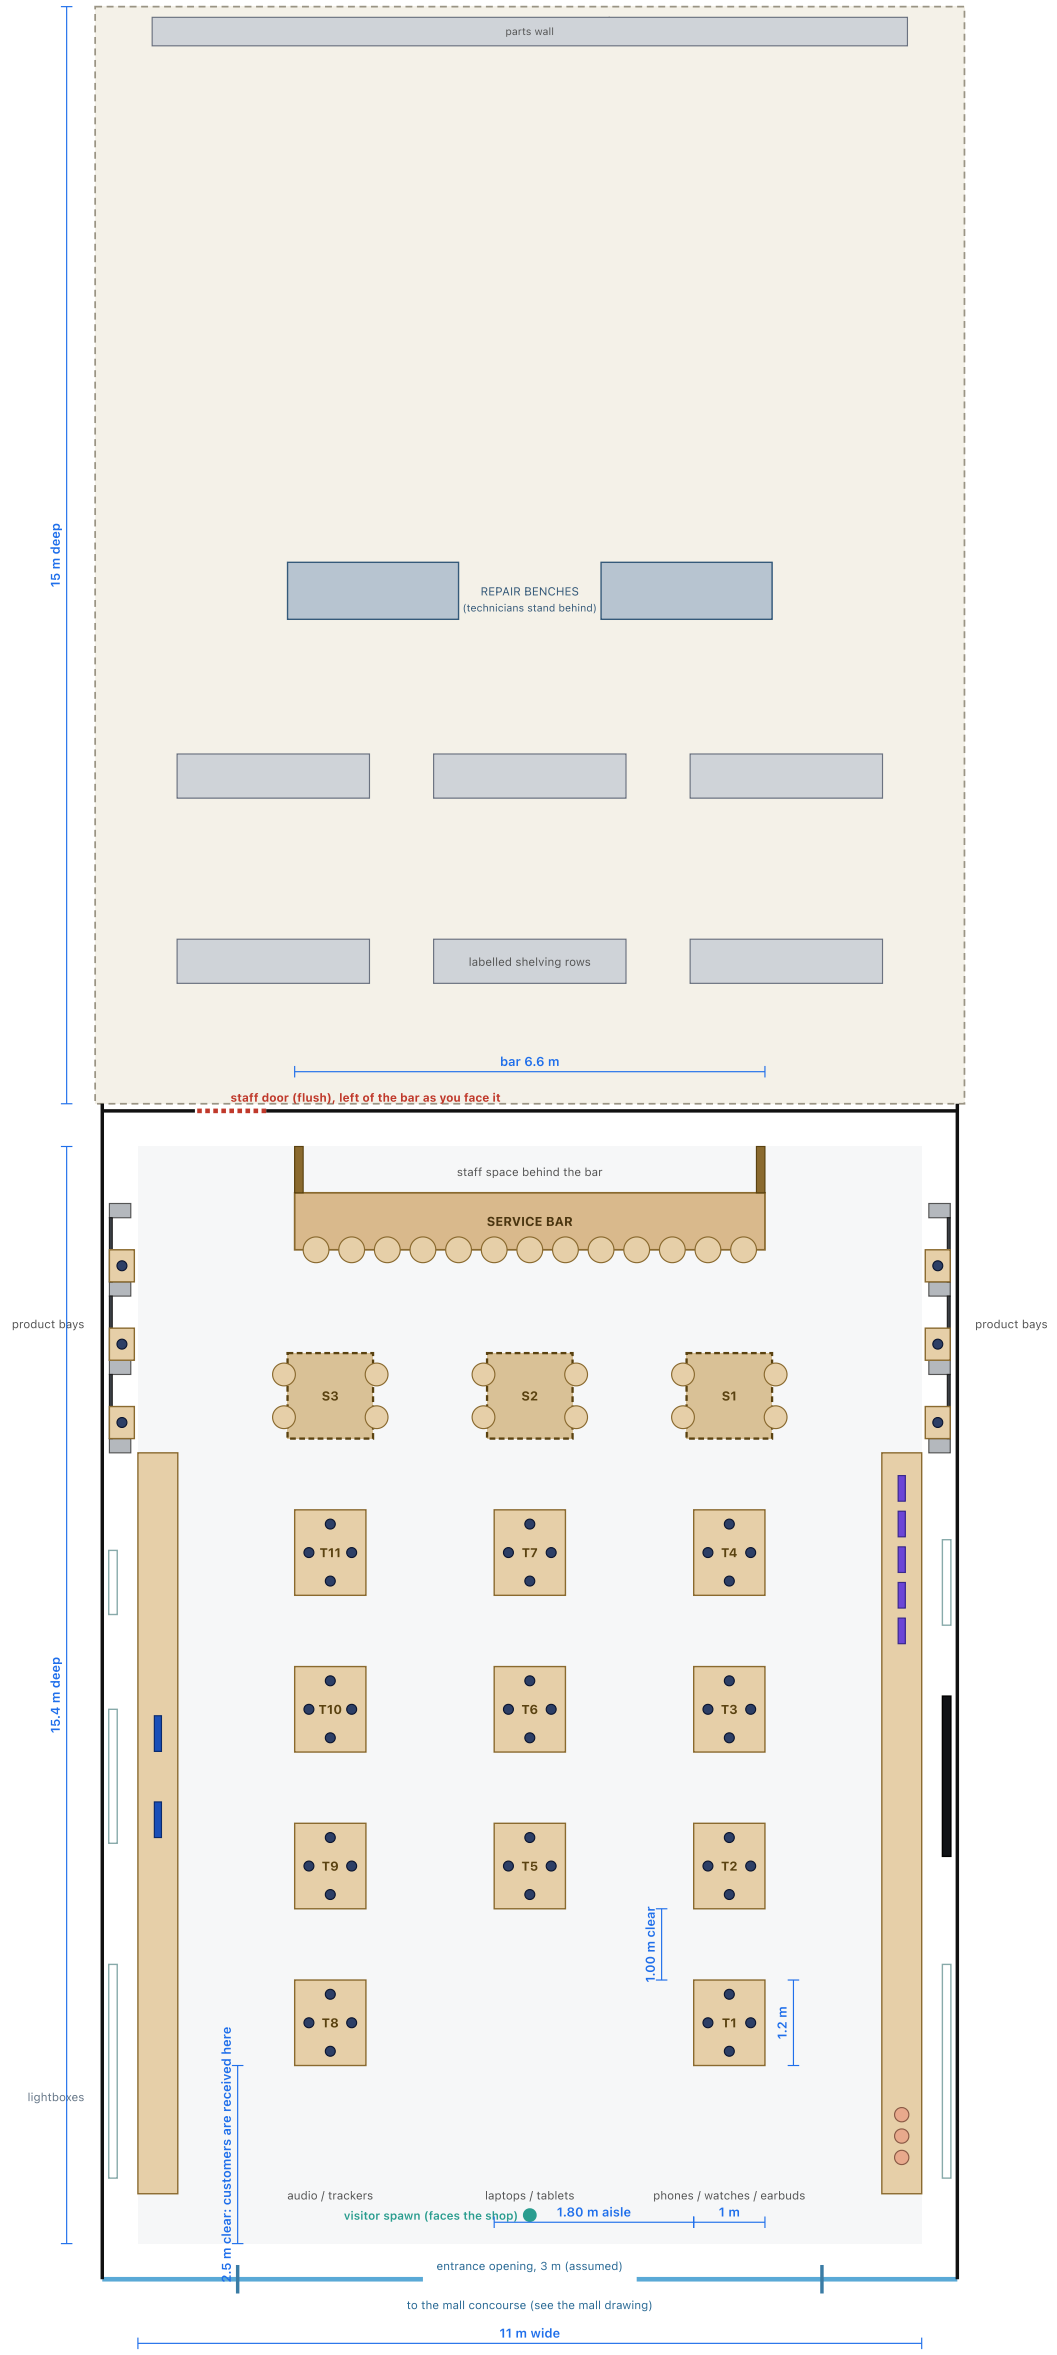

Ceiling 3 m. T = product table (1 x 1.2 m, one product per side). S = square service table (1.2 m side, no products, two stools each side, tucked under). Columns at x = -2.8, 0, 2.8. The 3 m wall height is from the references; the width and depth were enlarged on request (option A) so there is room to move between tables.
Assumed, not measurable: table length, the entrance opening, the back-room layout (your instruction: same footprint), the door width.

Top-down plan: the mall around the store


The mall around the store: concourse, shops, mezzanine and routes (metres; +x on the LEFT)

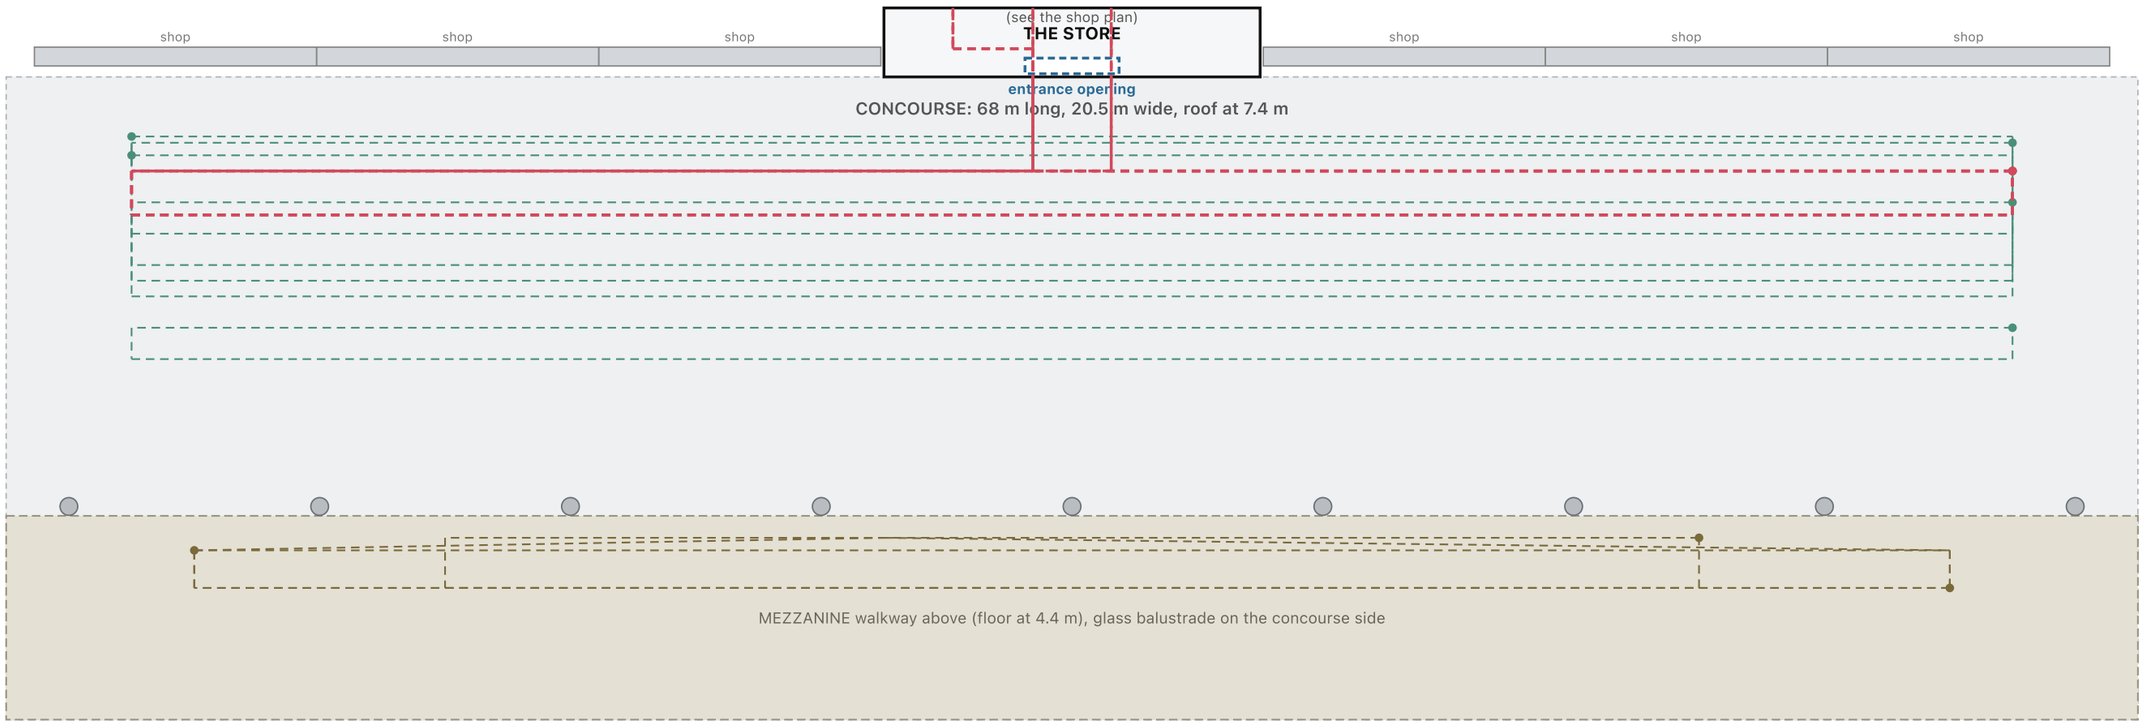


Green: people walking past (two stop to window-shop). Red: customers who come in through the opening, look at tables and leave. Olive: people on the mezzanine. Everyone is placed by the shared server clock, so all visitors see the same people in the same places. The mezzanine and neighbouring shops are not enterable.
Sizes of the concourse, the neighbours and the mezzanine are assumed; only the store itself comes from the reference photographs.

Walls: the side walls

1. LEFT WALL as you enter (the +x wall). Glass front on the left, back wall on the right.

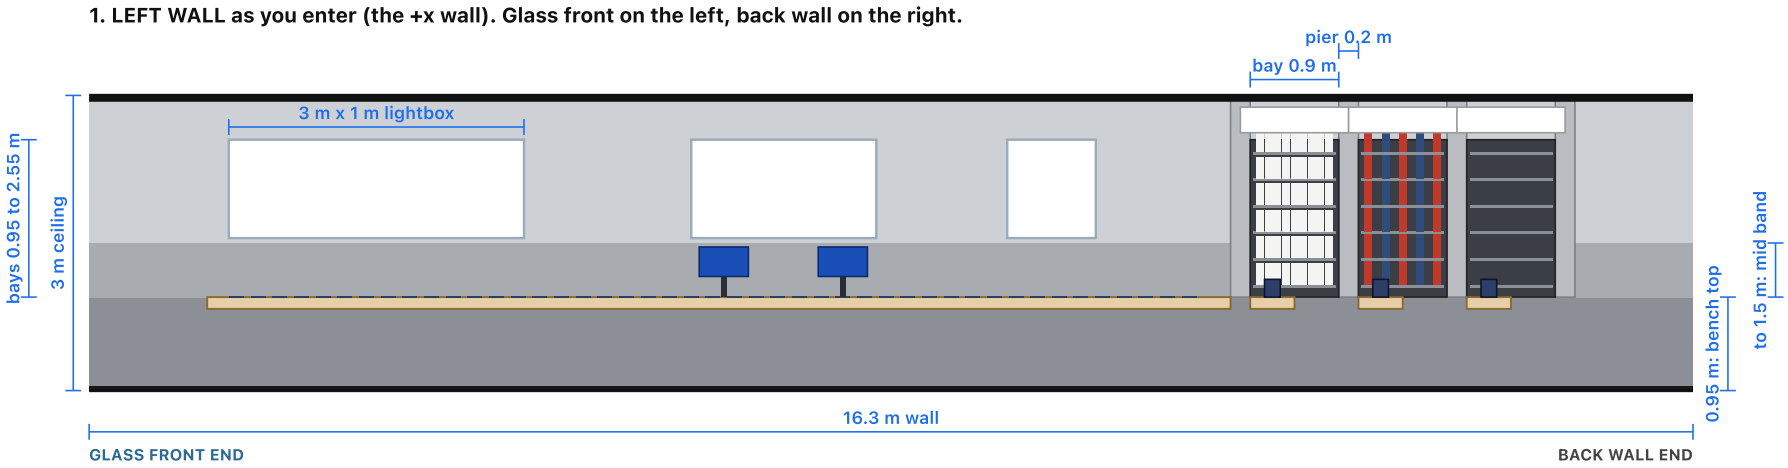


2. RIGHT WALL as you enter (the -x wall). Glass front on the right, back wall on the left.

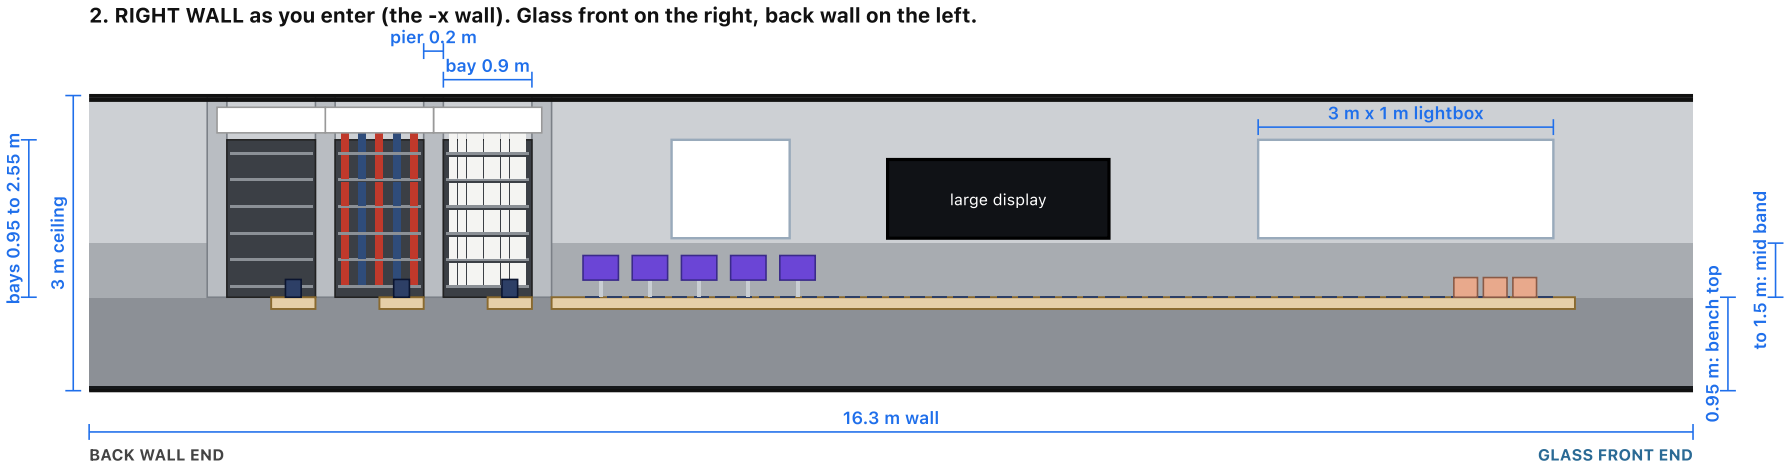


Walls: the back wall and the glass front

3. BACK WALL, shop side (z = +8.1), seen facing it. The +x side is on the left.

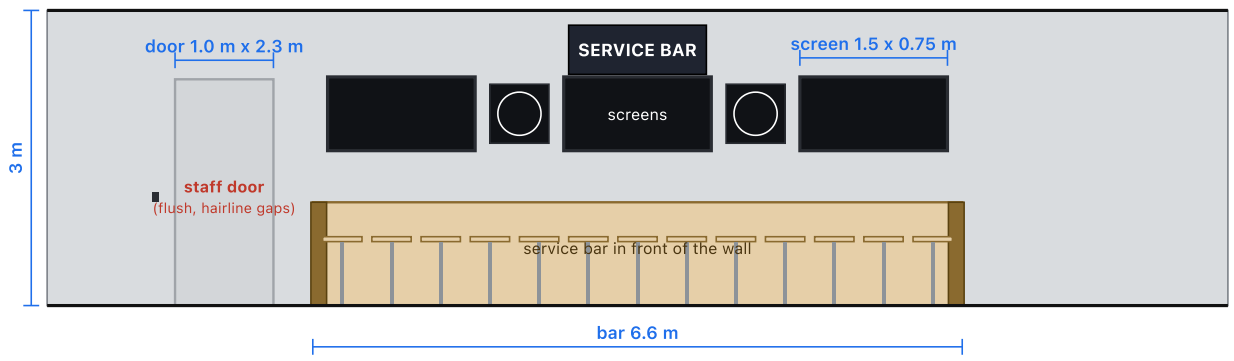


4. FRONT GLASS WALL (z = -8.2), seen from inside facing it. The +x side is on the right.

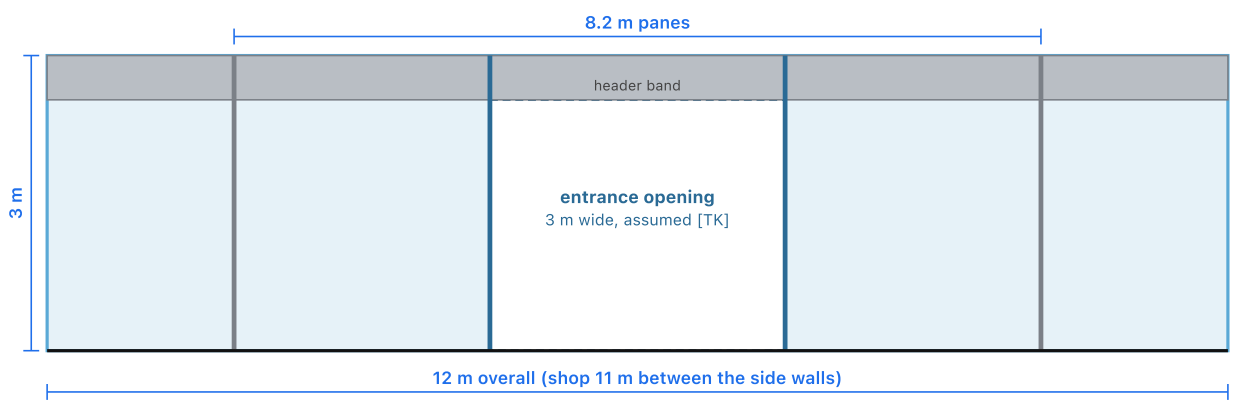

Ceiling and lights

Ceiling and lights, looking up from inside: +x wall on the LEFT, entrance at the bottom (metres)

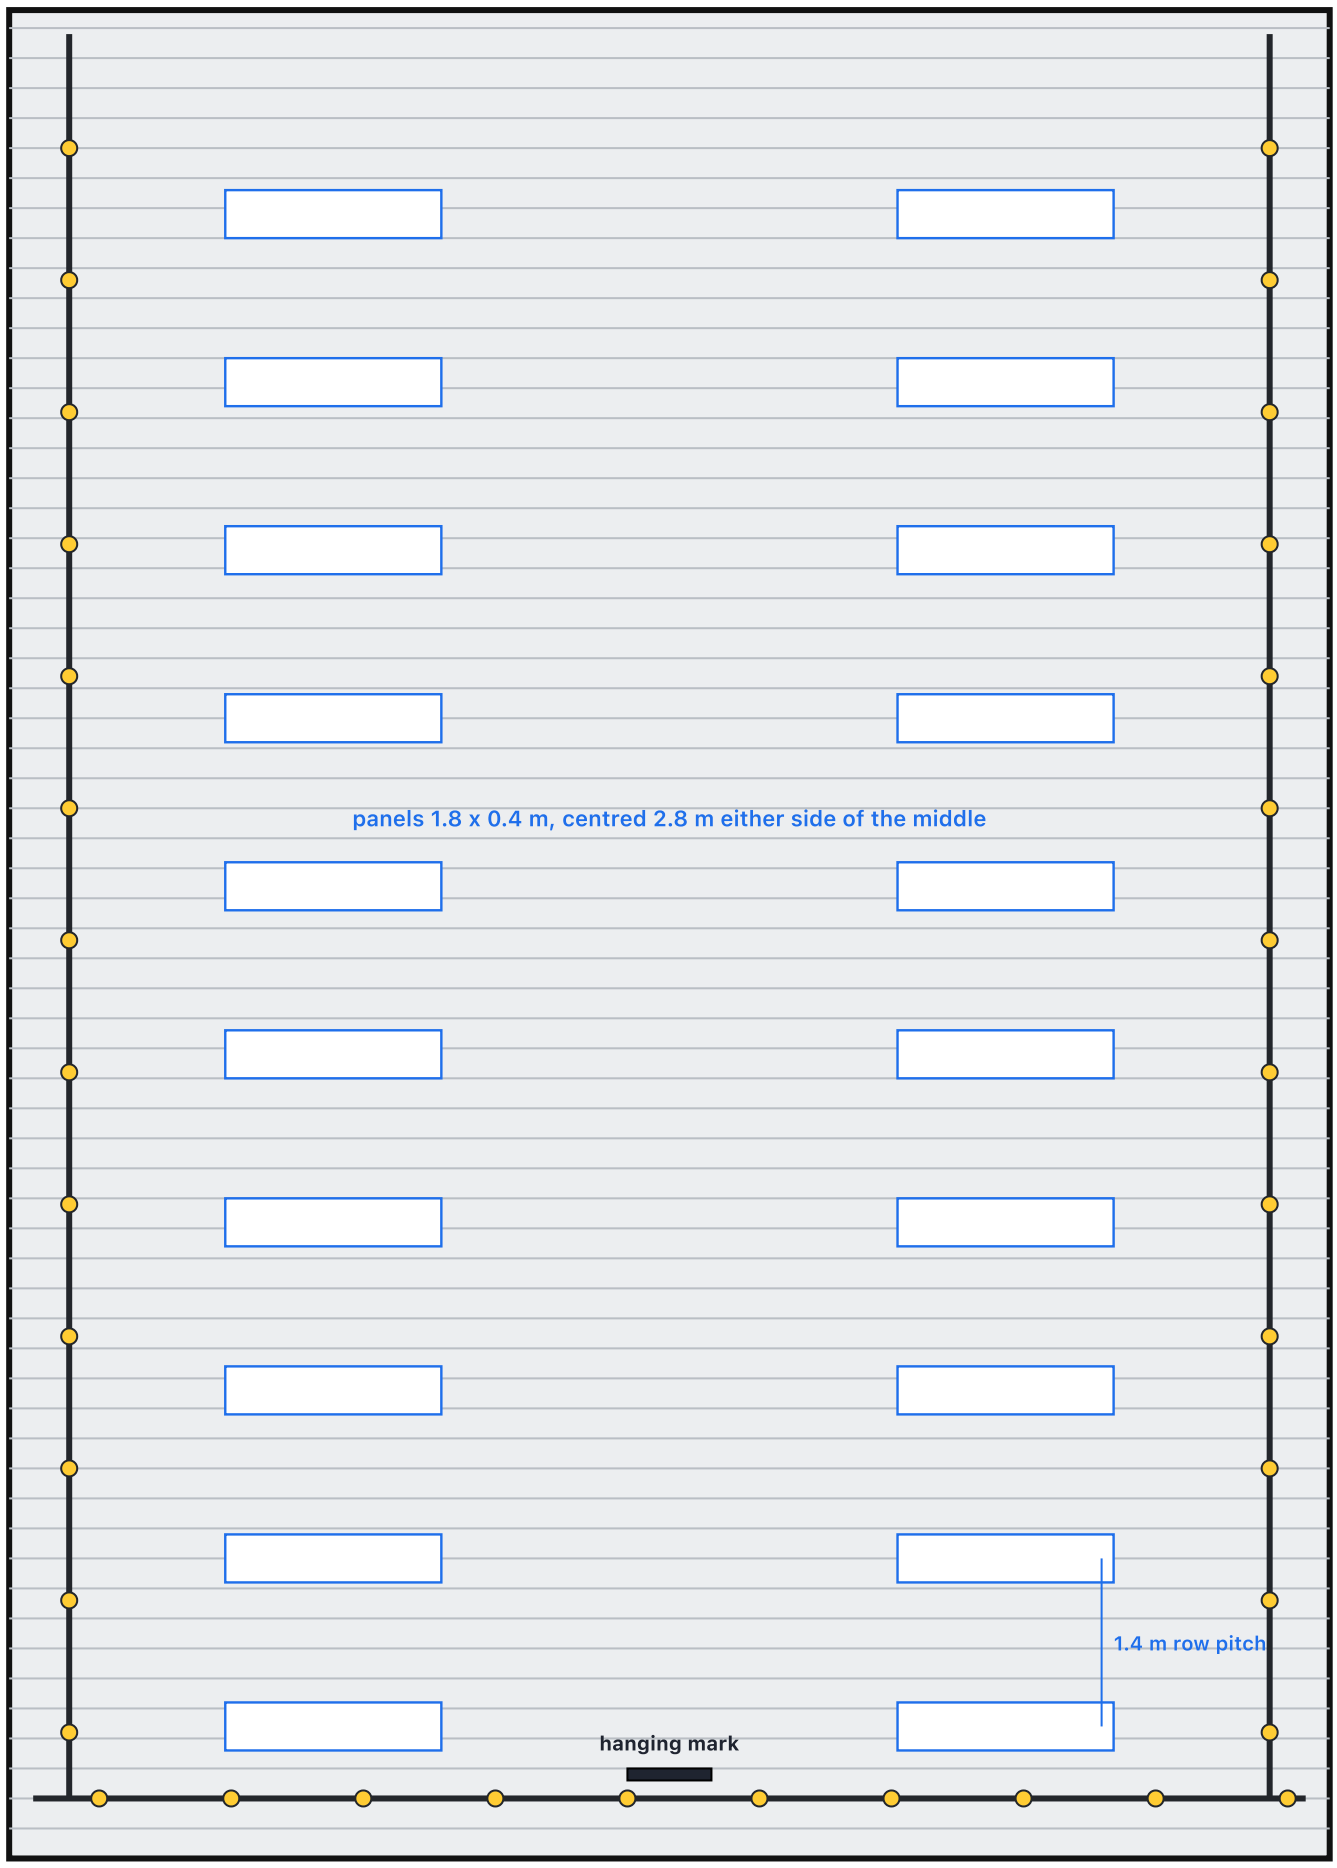

Slats run across the room (along x) every 0.25 m. Spots every 1.1 m on rails 0.5 m in from the walls.
Ceiling height 3 m; the rails sit at 2.96 m. Panel rows read from the front-on photograph; the exact count is an estimate.
The hanging mark is an original service mark, not anyone's logo.